

LIMINA

Du seuil à la ville

Works of Jaegyu LEE | 2026

Jaegyu LEE

Paris, France

Jaegyu_lee@esa-paris.net

Je considère que la rupture des liens entre les personnes est l'un des grands problèmes de notre époque, et qu'il s'agit avant tout d'une question urbaine. C'est d'ailleurs le sujet de mon mémoire de licence. Autrefois, la ruelle ou l'ombre du grand arbre du village étaient des lieux où l'on se saluait, où l'on s'arrêtait pour parler. La ville découpée en zones fonctionnelles, elle, se vide dès que l'activité cesse. L'architecture ne peut pas, à elle seule, recréer ces liens. Elle peut en multiplier les occasions, et faire qu'on s'arrête, qu'on reste, là où d'habitude on ne fait que passer. Ces occasions naissent souvent dans les seuils et les détails, comme un banc, une marche où s'asseoir ou une coursive assez large pour devenir un balcon commun.

C'est pourquoi je souhaite concevoir à toutes les échelles, de la poignée de porte à la ville, et donner à chacune une intention claire.

FORMATION	09.2024 - Présent	École Spéciale d'Architecture (ESA), Paris - Licence d'architecture
	03.2021 - 10.2021	Un semestre en Génie Civil Agricole, Université nationale de Kyungpook, Corée du Sud

EXPÉRIENCES	01.2026 - 02.2026	Clément Blanchet Architecture (Stagiaire)
	07.2025 - 08.2025	Habitat for Humanity Korea (Stagiaire)
	01.2022 - 10.2023	Service Militaire (Armée de l'Air)

COMPÉTENCES	Dessin / CAO	AutoCAD, QGIS
	Modélisation 3D	Rhino, Grasshopper
	Rendu	D5Render, Enscape
	Post-production	Adobe Photoshop, InDesign, Illustrator
	Bureautique	Microsoft Office (Word, Excel, PowerPoint)
	Soft Skills	Maquette physique, Dessin à la main, Croquis d'architecture
	Outils numériques	Python, automatisation Rhino/Grasshopper avec l'IA (outil TerrainLaser)

LANGUES	Français	Niveau B2 (Certification DELF obtenue en mars 2026)
	Anglais	Niveau professionnel
	Coréen	Langue maternelle

INTÉRÊTS	Voyage, Photographie, Baseball, Cuisine, Lecture & Écriture architecturale
----------	--

Sommaire

01

La ville en continuité

Stage _ 2026

02

La Seine des cultures

L2S2 Centre Culture

03

Habiter le changement

Projet personnel _ Logement collectif

La ville en continuité

Réinventer les liens entre infrastructures, paysage et quartiers





Année : 2026
Typologie : Projet urbain
Programme : Quartier mixte
Site : Rákossrendező, Budapest, Hongrie
Cadre : Projet d'agence — Stage
Équipe : Clément Blanchet Architecture
FBIS Architects
Gustafson Porter + Bowman
Participation : Assistant de projet

Pendant mon stage j'ai travaillé sur le masterplan du site ferroviaire de Rákossrendező à Budapest. Les voies ferrées y séparent les quartiers. Le projet les recoud autour d'un parc linéaire et laisse les traces existantes guider un quartier mixte construit en cinq phases sur environ vingt-cinq ans. C'était mon premier projet à l'échelle de la ville. J'y ai réalisé le graphisme du masterplan et j'ai compris comment se fabrique un plan d'urbanisme.

Comment reconnecter un territoire fragmenté sans effacer les traces de la ville existante ?



Maquette réalisée par un maquettiste professionnel

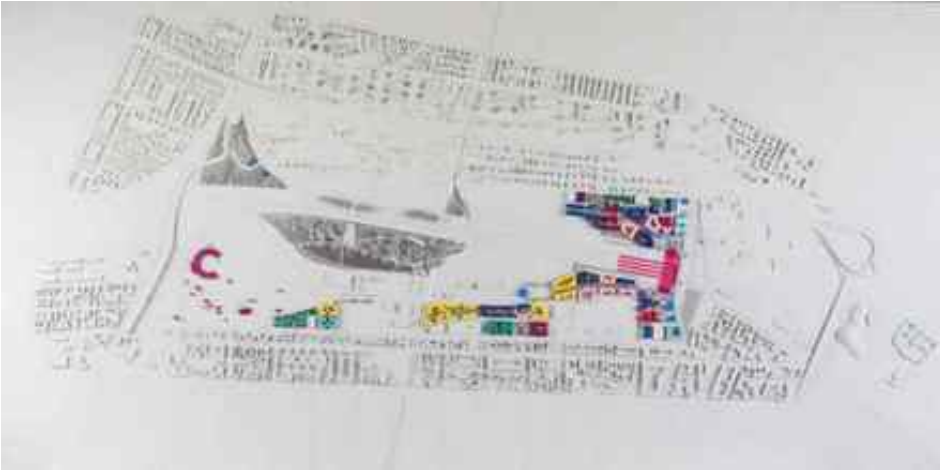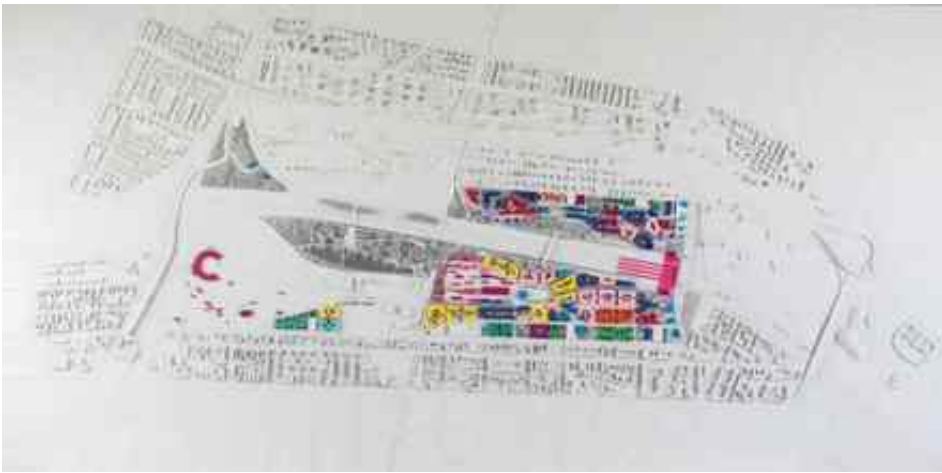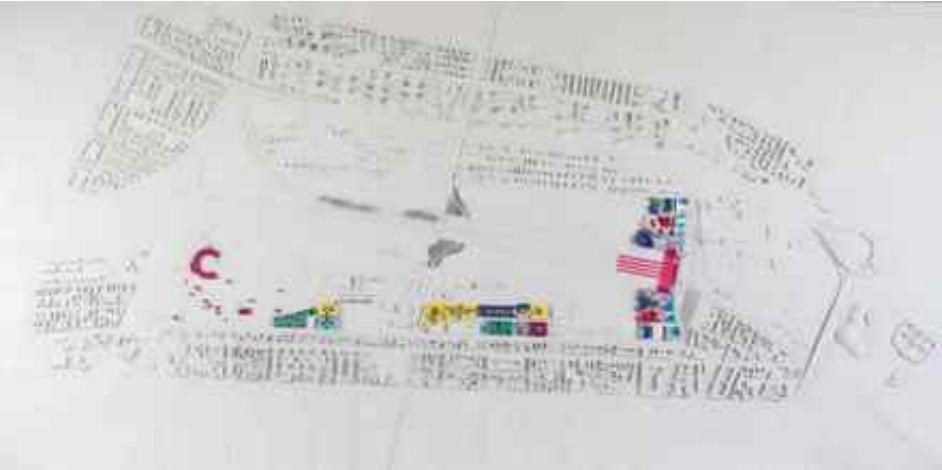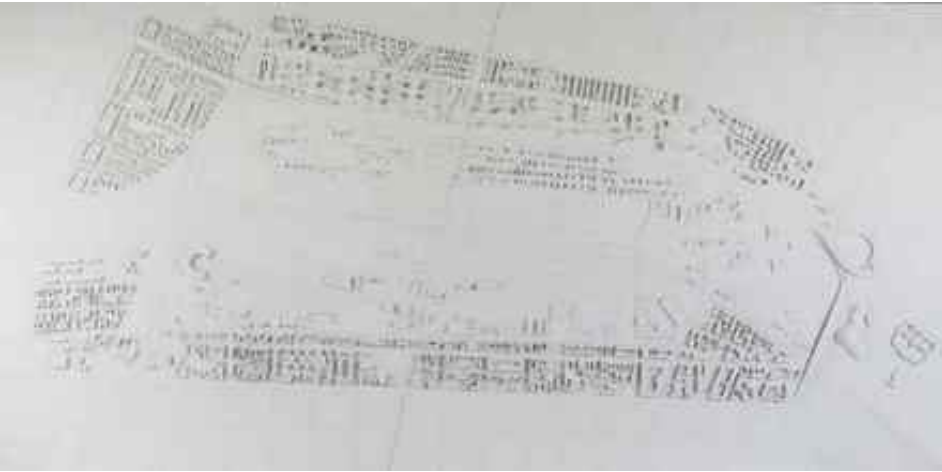


Maquette réalisée par un maquettiste professionnel

STRUCTURE URBAINE — Articuler les différentes échelles

Les densités se concentrent autour de la gare et des nouveaux quartiers résidentiels. Les hauteurs et les typologies varient selon la proximité des grands pôles. Entre ces quartiers le parc linéaire fait le lien.

PHASAGE — Construire la ville progressivement

Le quartier se construit en cinq phases sur environ vingt-cinq ans. Tout part des infrastructures existantes. La ville s'étend ensuite autour de la gare puis gagne les espaces publics et les quartiers résidentiels. Le parc et les extensions viennent en dernier.

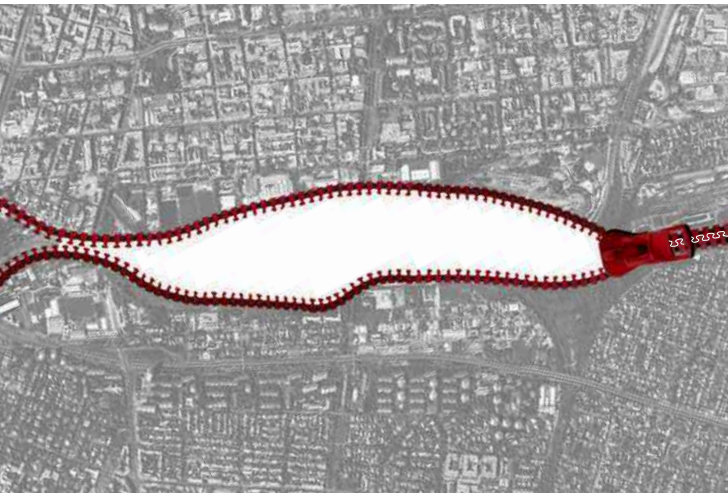


I. Recoudre la ville

L'emprise ferroviaire a longtemps coupé la ville en deux. Elle devient une armature paysagère que l'on traverse en plusieurs points et qui raccroche les quartiers voisins au reste du territoire de part et d'autre des voies.




II. Créer la diversité dans l'unité

Les typologies et les hauteurs changent d'un îlot à l'autre et les espaces publics aussi. Une même composition les réunit. Chaque partie du quartier garde son caractère sans perdre la cohérence de l'ensemble du projet.

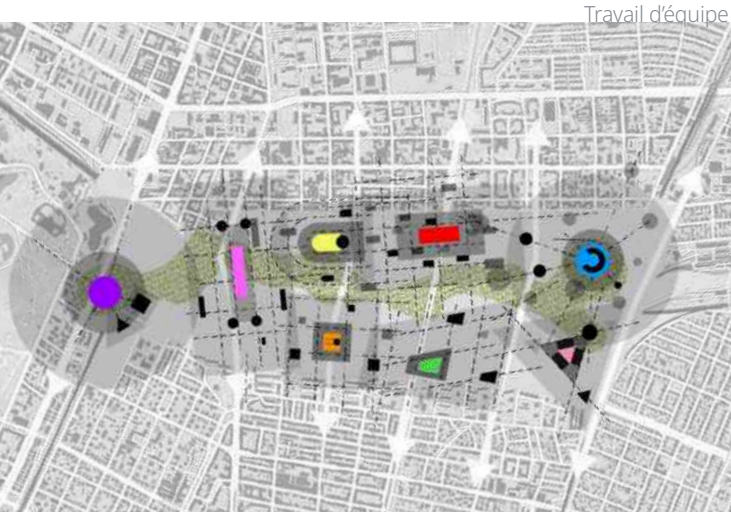

III. Réinterpréter l'identité de Budapest

Le projet puise dans l'histoire de Budapest. On y retrouve la générosité de ses espaces et son rapport au paysage. Ces qualités sont réinterprétées pour que le territoire change au fil des phases sans perdre son identité.

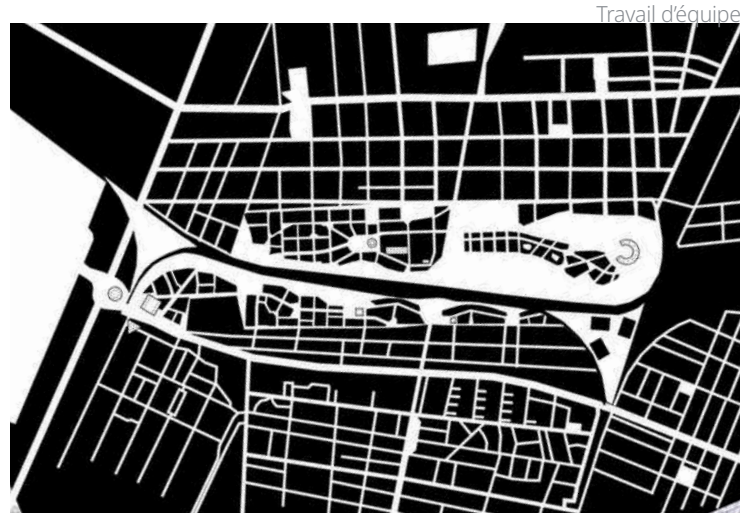


IV. Révéler les connexions historiques

Les anciens tracés et les axes de mobilité existants sont d'abord relevés puis réactivés. Ils dessinent les nouvelles connexions entre les quartiers et rattachent le projet à la trame de la ville qui l'entoure.




V. Créer des mémoires collectives

Les places et les jardins sont dessinés pour les usages de tous les jours à l'échelle du piéton. On s'y arrête et on s'y croise. C'est ainsi qu'une mémoire collective peut se former avec le temps entre les habitants.

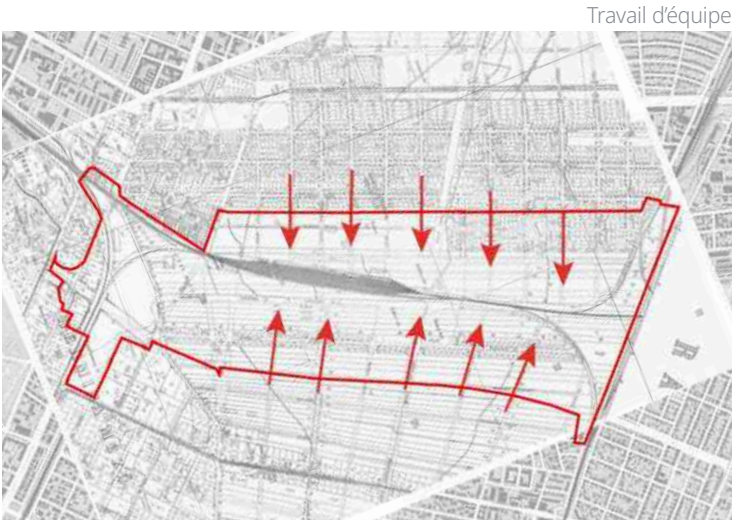


VI. Habiter la ville des 15 minutes

Les logements et les services sont répartis avec les équipements et les loisirs pour que la vie quotidienne reste proche. Les parcours piétons et les transports publics relient ces usages à l'échelle du quartier.

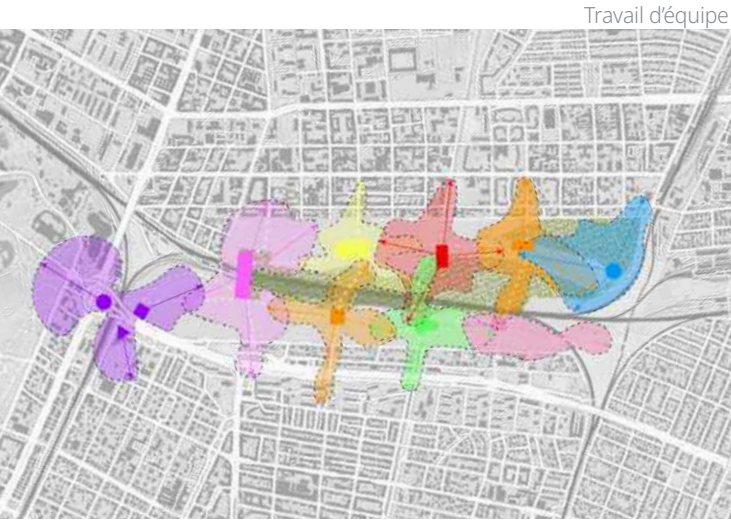

VII. Structurer la ville par le parc

Le parc linéaire porte l'essentiel des espaces publics et relie les quartiers entre eux. Du paysage aux espaces bâtis la transition se fait par étapes et l'on passe doucement du domaine public au domaine privé sans frontière nette.

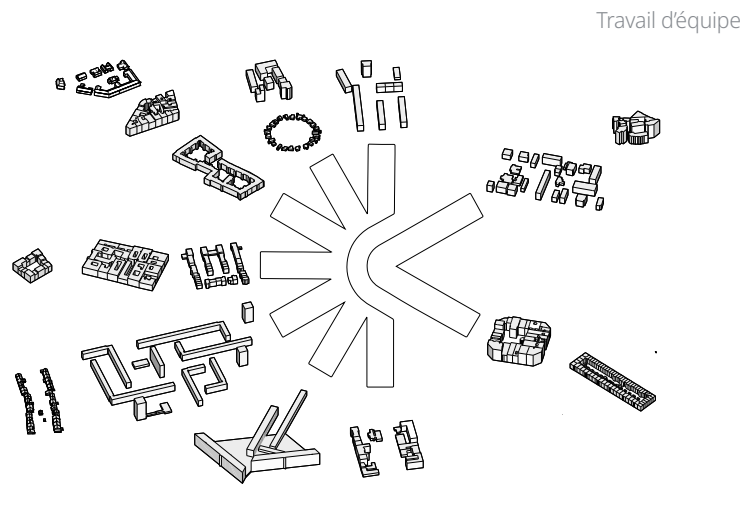

VIII. Réinterpréter l'héritage urbain européen

Le masterplan reprend ce qui fait la ville européenne. La densité et la mixité des usages vont avec la marche à pied et une vie publique active. Le quartier repose sur des principes qui ont fait leurs preuves.

Conception en équipe · Mise en forme graphique personnelle



LÉGENDE

1

2

3

4

5

Développement futur

Zone centrale

Zone d'intervention

Périmètre du projet

Toiture végétalisée

Toiture accessible

Zone scolaire

Équipement sportif

P Parking silo

6

12

13

La Seine des cultures

Du livre à l'outil, du papier à la terre


Année : Printemps 2026

Typologie : Bibliothèque + espace public hybride

Programme : Lecture, atelier, cantine, archive

Site : Patinoire de Colombes, Colombes

Concept : Réemploi, culture et écologie

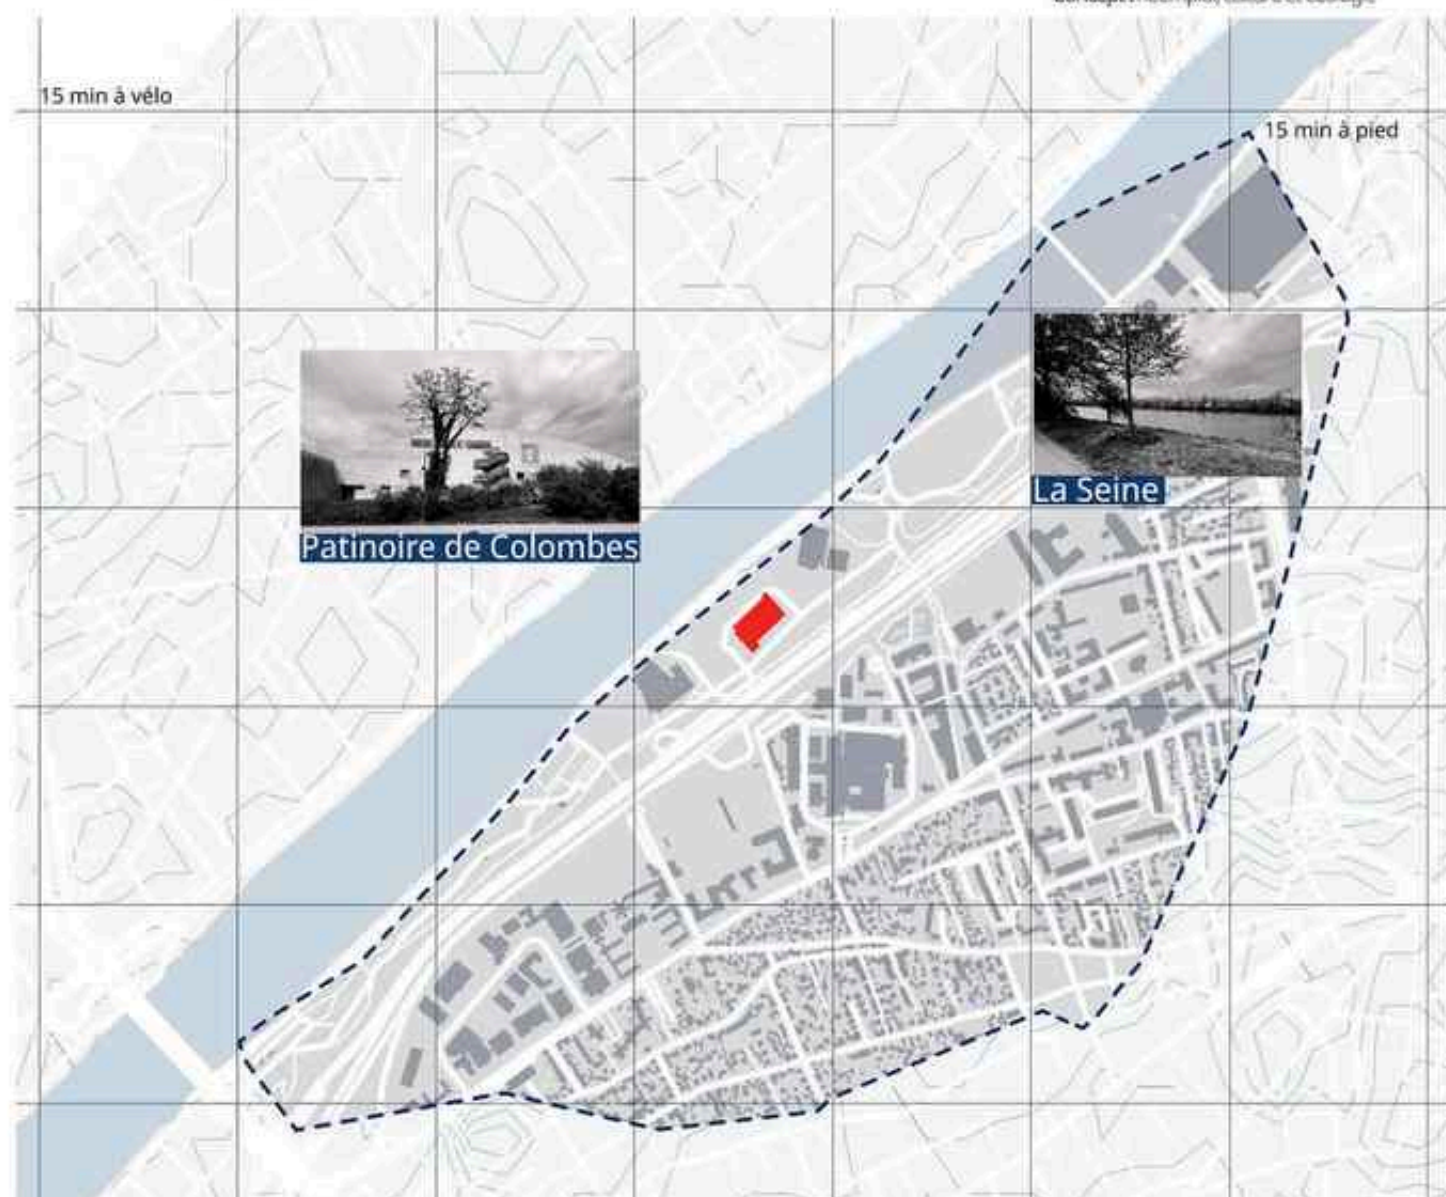

Pourquoi ce site ?

: Nécessité Territoriale



Six écoles sans bibliothèque dans un rayon de 15 minutes révèlent un besoin culturel partagé et un manque d'équipements à l'échelle du quartier.

FRAGMENTATION URBAINE

: Fractures et continuités



Malgré les ruptures de l'autoroute et de la Seine, le site capte et guide naturellement les flux.

L'ÎLOT VERT

: Une enclave paysagère



Isolé par l'autoroute et la Seine, le site forme aujourd'hui une enclave paysagère au sein du tissu urbain environnant. Sa forte présence végétale lui confère le caractère d'un véritable « îlot vert ».

USAGES

: À l'interface entre activités et habitat



Le site s'insère entre plusieurs polarités tertiaires, entourées principalement par des secteurs résidentiels. Cette position crée une interface entre les activités urbaines et les quartiers d'habitation.

Le territoire inondable

: La Seine et le risque d'inondation



La proximité de la Seine expose le site à un risque d'inondation. Les zones inondables soulignent la vulnérabilité du territoire face aux variations du niveau de l'eau, lors des épisodes de crue.

TRAME VERTE

: Un îlot vert au cœur du tissu urbain



Les espaces verts se concentrent principalement autour du site et le long de la Seine, créant une situation paysagère privilégiée et une continuité écologique au sein du tissu urbain.

01 — L'ÎLE



Un ancien territoire insulaire façonné par la Seine.

02 — LE REMBLAEMENT




Le remblaiement rattache le territoire à la ville.

03 — L'URBANISATION



L'urbanisation et les infrastructures fragmentent le territoire.

04 — L'ÎLOT VERT

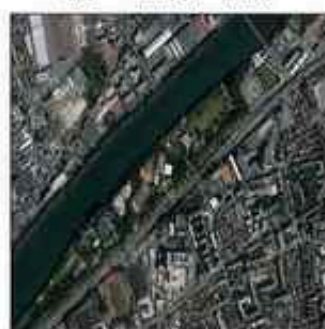

Un îlot paysager préserve au cœur de la ville.

À l'origine territoire alluvial, ce site s'est transformé en un espace vert aujourd'hui isolé par la Seine et les grandes infrastructures, formant une véritable « île verte ». Malgré six établissements scolaires à 15 minutes à pied, le quartier manque d'équipements culturels partagés. Ce potentiel invite à créer une nouvelle polarité socioculturelle ouverte sur la ville.

Comment transformer cette enclave paysagère, isolée par les infrastructures métropolitaines, en un nouveau territoire culturel et écologique ouvert sur la ville ?





RÉEMPLOI & CYCLE DU SAVOIR

PROGRAMME — Le cycle du savoir

Tout part de la bibliothèque, où l'on vient apprendre. Ce savoir est mis à l'épreuve au jardin, à l'atelier et à la cantine, là où l'on cultive, fabrique et cuisine. Les usagers consignent ces expériences dans l'espace archive, ouvert au coworking, et en font des livres. Ces livres rejoignent les rayons de la bibliothèque, et le cycle recommence.

COMPOSITION — De l'existant au paysage


Le projet garde la charpente de la patinoire et retire une partie des façades et de la toiture pour ouvrir le bâtiment sur le paysage. Une rampe mène au rez-de-chaussée, où un sas vitré marque le passage de l'extérieur à l'intérieur. L'ancienne piste de glace devient un jardin d'eau qui recueille la pluie.

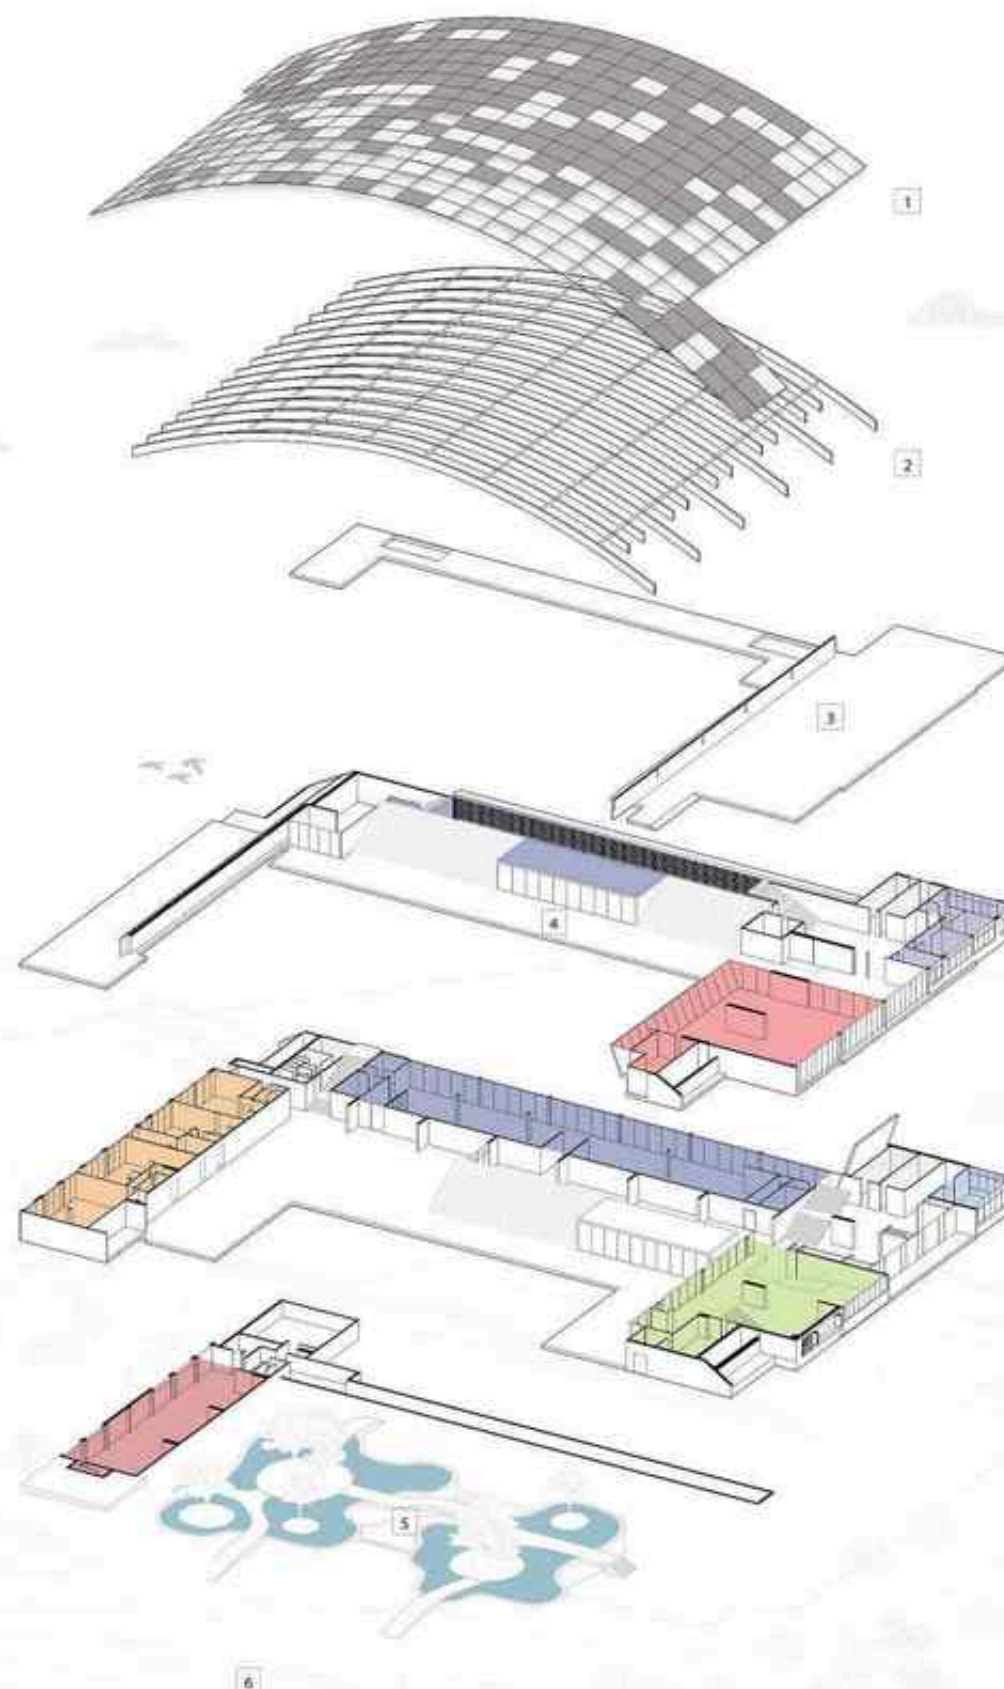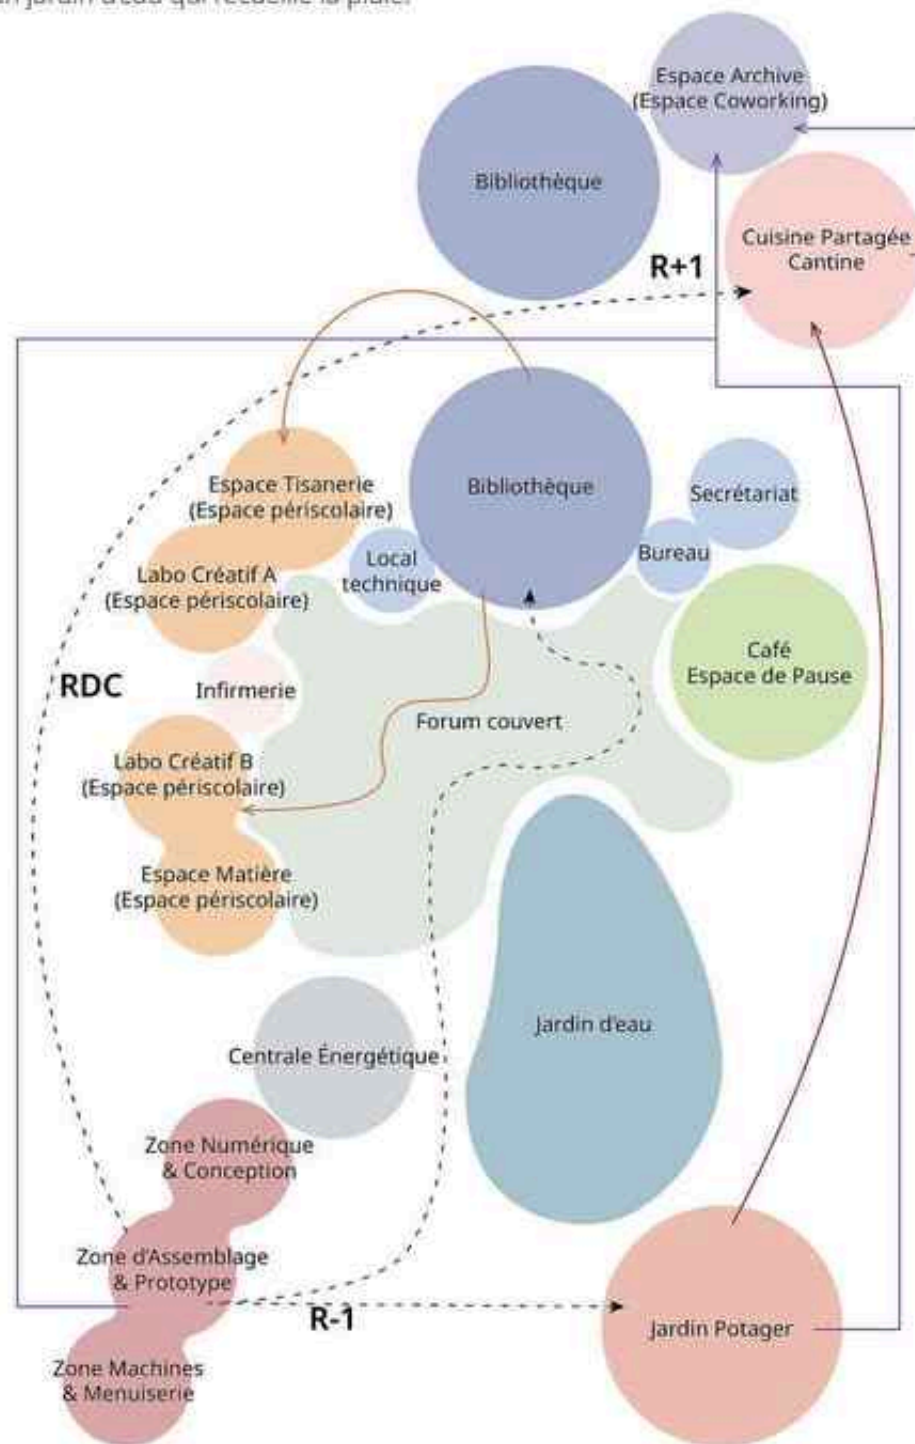

LÉGENDE

- 1 Enveloppe en gradient de densité (Zinc - Gris foncé / Vitrage - Gris clair / Vide)
- 2 Structure de charpente existante
- 3 Terrasse
- 4 Forum couvert
- 5 Jardin d'eau
- 6 Jardin potager

Déconstruction sélective

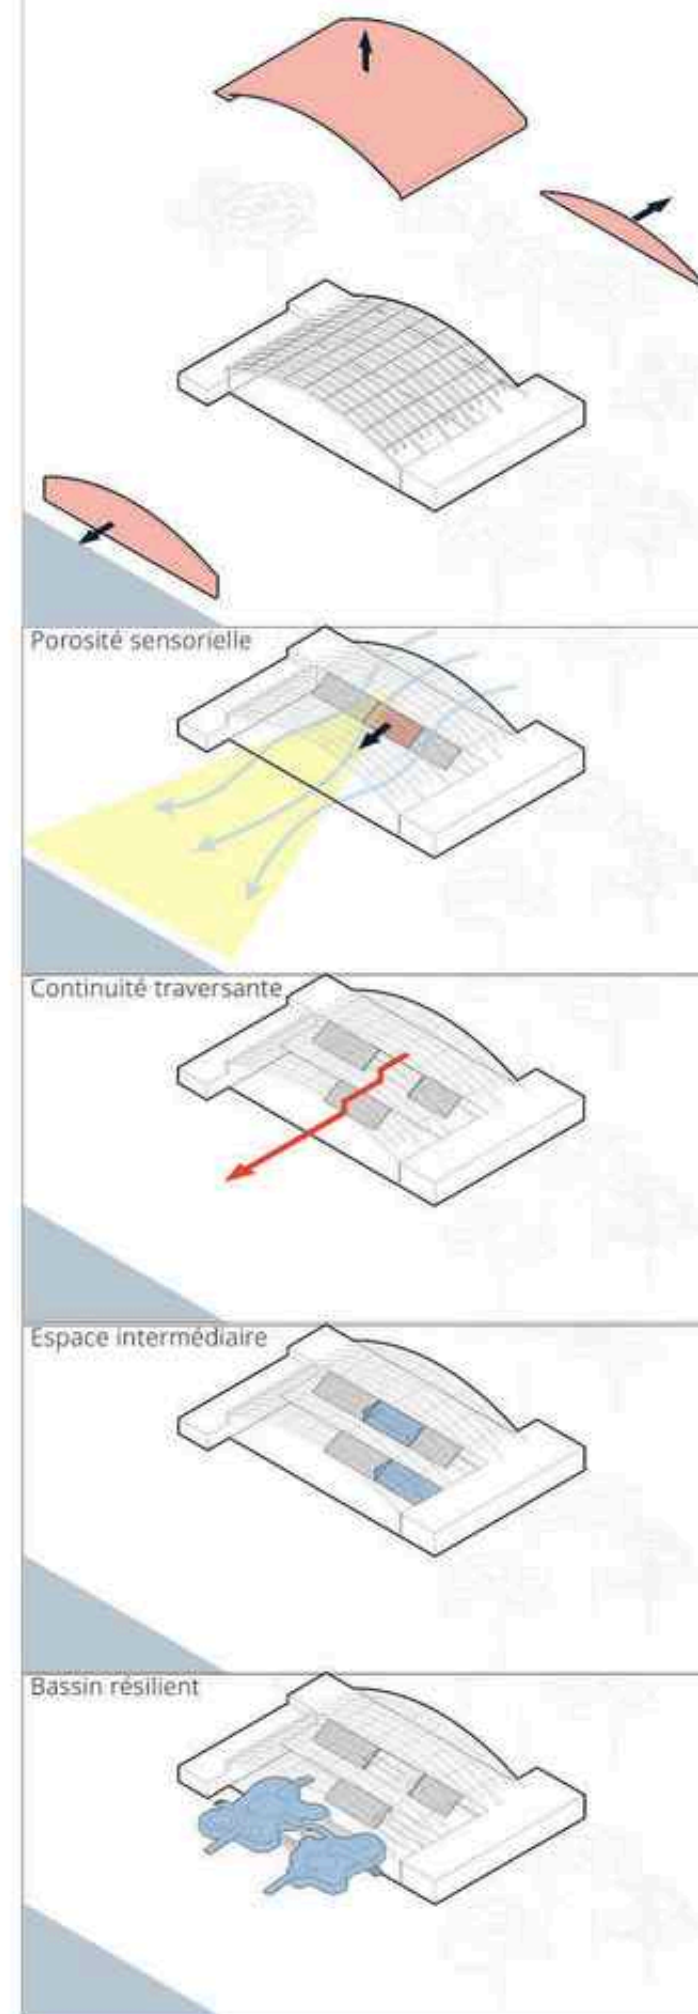


PLAN MASSE — Du bâtiment au paysage

Le site est pris entre la Seine et l'autoroute à côté d'un complexe sportif et d'une piscine. Il se trouve en zone inondable. L'ancienne patinoire reste à sa place mais se tourne désormais vers le fleuve. Entre le bâtiment et la berge s'étend le potager. Des chemins traversent les jardins jusqu'aux bassins.



LÉGENDE

- 1 La Seine
- 2 Complexe sportif
- 3 Jardin potager
- 4 Piscine
- 5 Autoroute


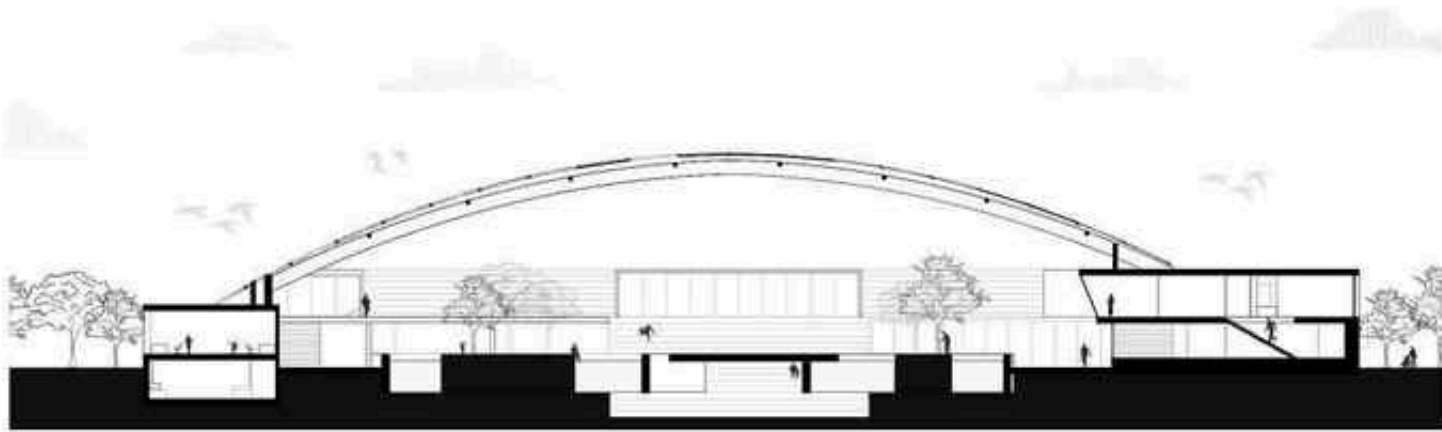


TOPOGRAPHIE & CONTINUITÉ

Le bâtiment comme prolongement du paysage


Le projet refuse la rupture entre le bâtiment et son paysage. La rampe et les variations de niveau prolongent le sol à travers l'architecture. On entre progressivement par le sas vitré et l'on retrouve le paysage depuis les espaces publics.

Les trois coupes suivent ce passage du dehors au dedans. Sur la première on voit la structure existante avec ses poutres principales en bois lamellé-collé. La deuxième montre le bâtiment ouvert sur l'extérieur. Avec la troisième le sol s'enfonce peu à peu jusqu'au jardin d'eau installé dans l'ancienne piste de la patinoire.

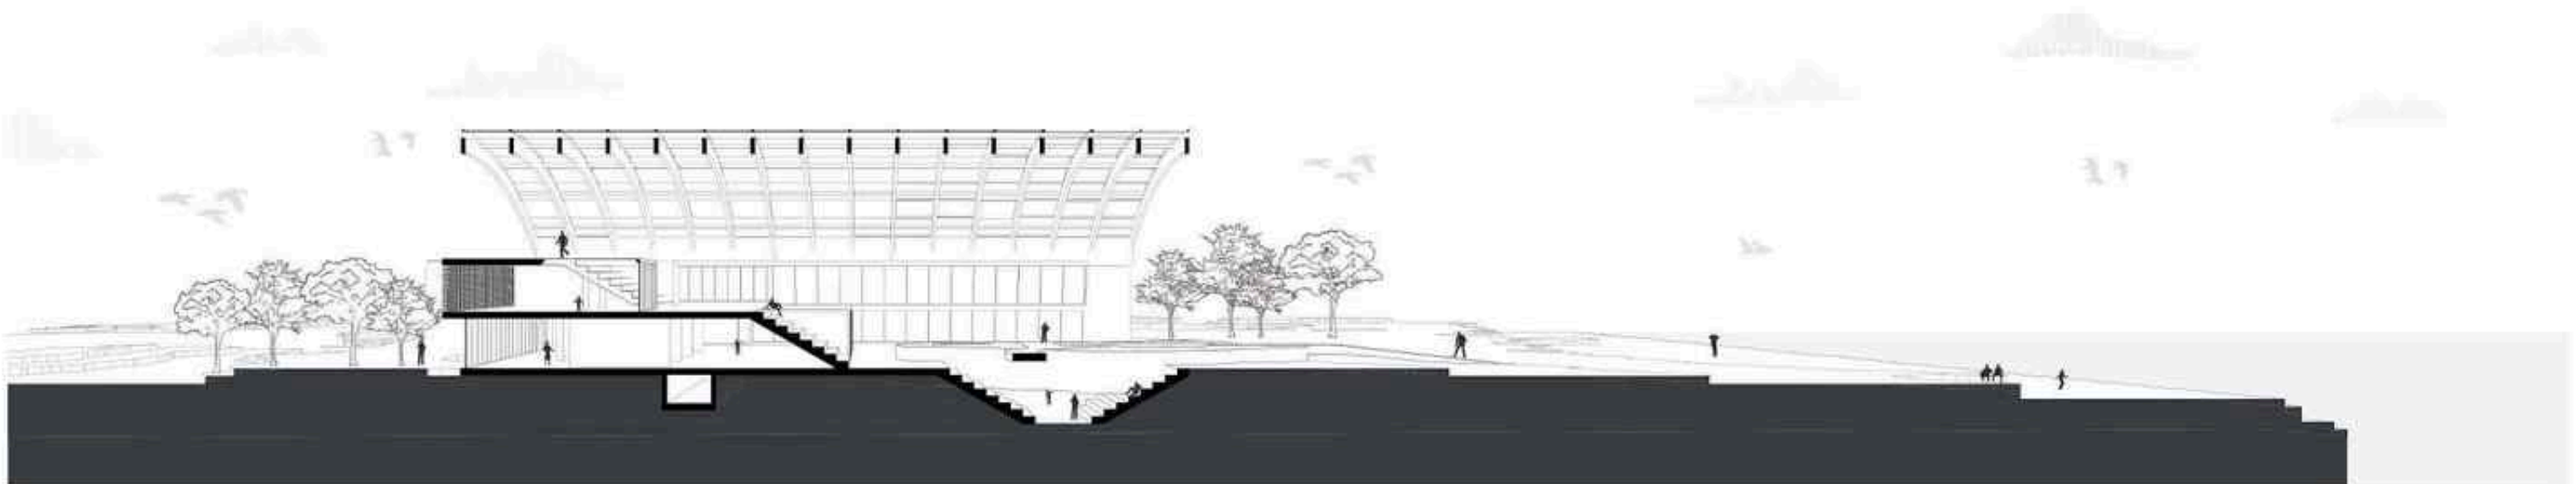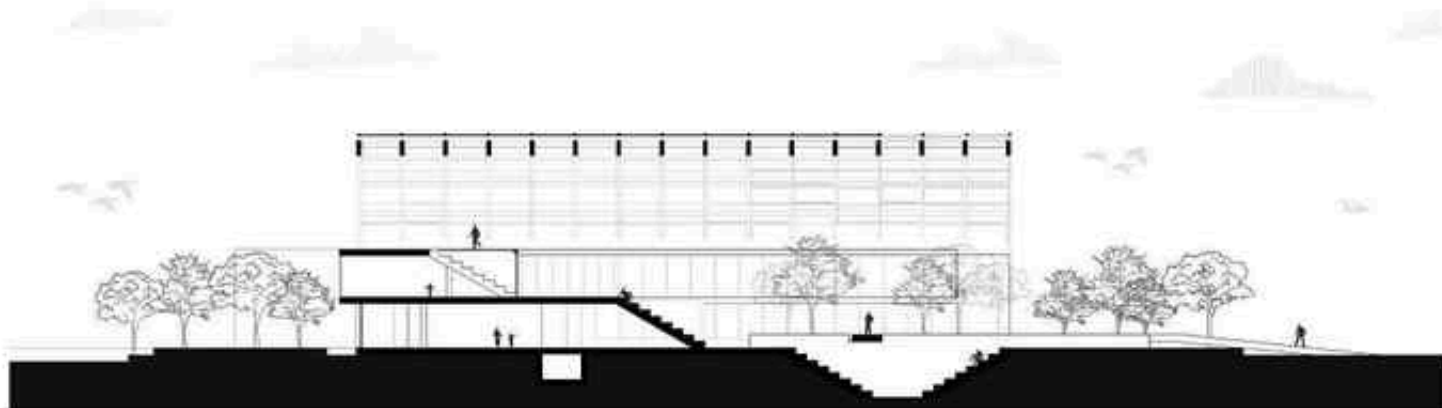


**STRUCTURE EXISTANTE
ET NOUVELLE ENVELOPPE**

On retire l'ancienne couverture de la toiture mais on garde les poutres principales en bois lamellé-collé ainsi que les poutres secondaires en bois. C'est sur cette charpente conservée que vient se poser la nouvelle enveloppe. Elle suit la trame d'origine de la structure et chaque trame reçoit deux modules en zinc, en verre ou laissés ouverts. Le zinc reste opaque et protège l'intérieur des intempéries tandis que le verre fait entrer la lumière naturelle sans laisser passer la pluie. Les modules ouverts jouent un autre rôle. Ils laissent entrer l'air et la lumière mais aussi la pluie qui tombe jusqu'au jardin d'eau du niveau inférieur. L'ordre de l'ancienne charpente reste lisible sous un toit plus ouvert et adapté à ses nouveaux usages.

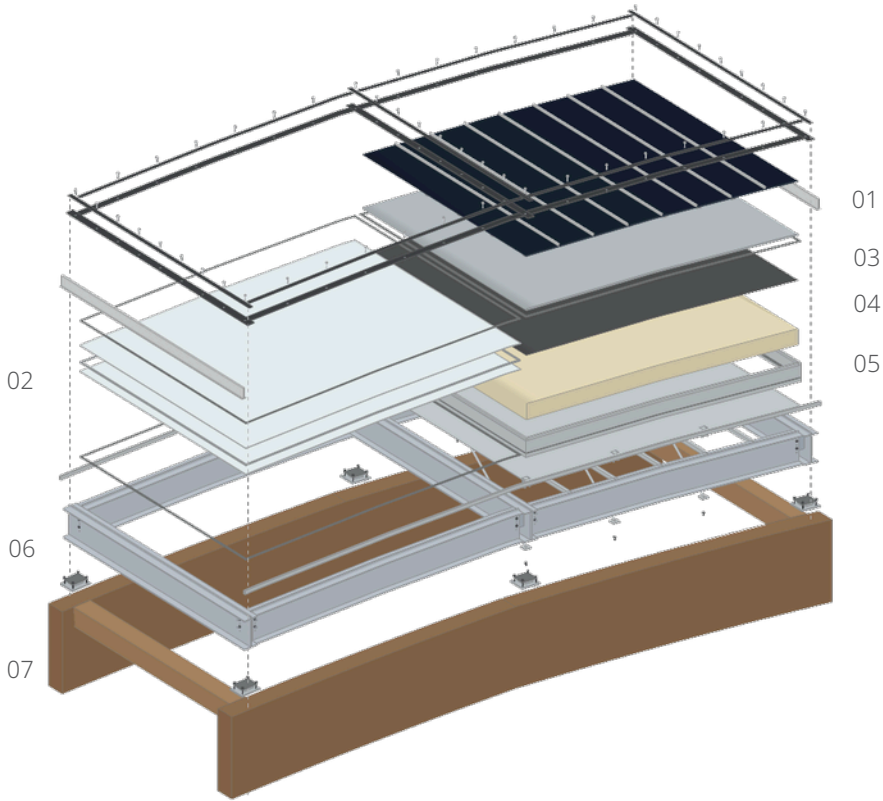


- 01 Panneaux photovoltaïques
- 02 Vitrage de toiture
- 03 Tôle d'acier support
- 04 Membrane d'étanchéité
- 05 Isolation thermique
- 06 Ossature métallique secondaire
- 07 Poutres principales existantes

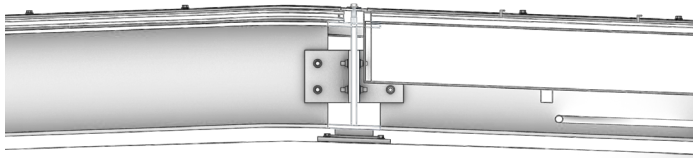

GESTION ET RÉUTILISATION DE L'EAU DE PLUIE

La pluie suit ici un parcours visible qui rappelle que ce site a longtemps été façonné par la Seine. La grande toiture courbe en zinc et en verre protège l'intérieur des intempéries et conduit l'eau vers ses deux extrémités. Des gouttières et des conduites intégrées la descendent jusqu'au niveau inférieur du bâtiment. Une autre partie tombe au milieu de l'espace central par les ouvertures laissées entre certains modules. Les usagers la voient tomber du ciel les jours de pluie. Les deux parcours se rejoignent dans le jardin d'eau qui occupe l'ancienne fosse de la patinoire. L'eau y est stockée et filtrée puis réutilisée sur place pour arroser le potager voisin.

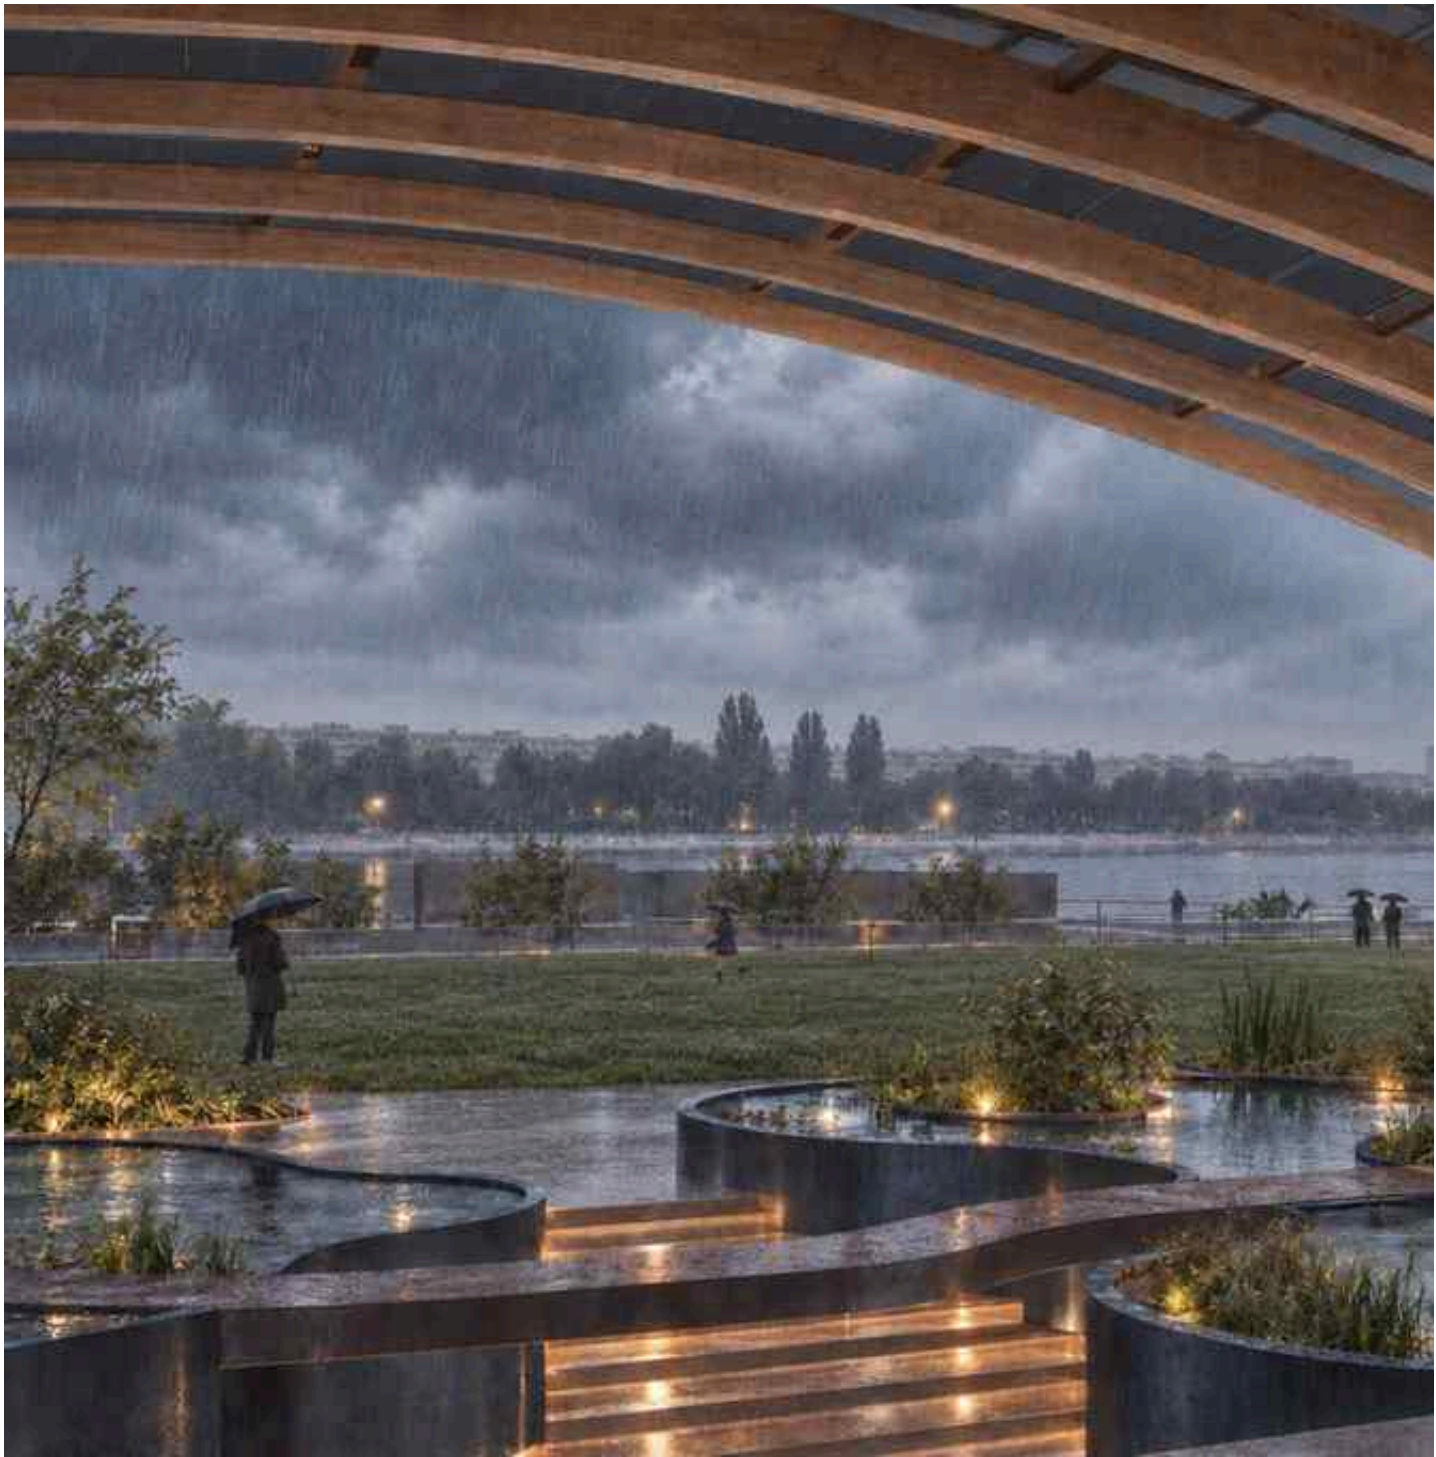

Habiter le changement

Modularité, porosité et vie collective

Projet personnel

Typologie : Logement collectif + espace partagé

Programme : Logements + équipements de quartier

Site : Romainville (93), France

Concept : Trame fixe, logement évolutif, seuils partagés

À Romainville les logements reposent sur une trame de 3,30 m. On déplace les cloisons pour réunir deux unités ou pour les séparer sans toucher à la structure. Le logement change de taille avec ses habitants du studio au T3. Le jardin d'hiver agrandit l'espace de vie et la coursive large de 3 m devient un balcon commun avec ses bancs et ses plantes. Les voisins se partagent un potager au rez-de-chaussée et un autre sur le toit. On s'y retrouve sans avoir à se donner rendez-vous.

Comment un logement peut-il suivre les étapes d'une vie et s'agrandir ou se réduire sans que l'on touche à sa structure ?



PLAN MASSE Organiser le vide collectif




Plusieurs volumes de logements se répartissent autour d'un jardin commun avec des bancs et un potager. Entre eux les bâtiments s'interrompent et l'îlot s'ouvre sur la rue par une suite de passages et de petits jardins partagés. C'est le vide du centre qui tient tout l'ensemble du projet.



RDC Traverser l'îlot

Au rez-de-chaussée les passages prolongent la rue jusqu'au grand jardin central. Les circulations traversent les bâtiments de part en part et l'îlot ne se referme pas sur lui-même. Les entrées des logements et les équipements de quartier comme la médiathèque ou la laverie-café donnent sur ces passages qu'on emprunte tous les jours.

R+1 La coursive comme rue habitée


À l'étage les coursives font le tour du jardin intérieur et desservent tous les logements. Elles font 3 m de large et accueillent des bancs et des plantes en pot. On y passe pour rentrer chez soi et on s'y arrête un moment pour parler à un voisin. Chaque coursive devient un balcon commun à tout l'étage.

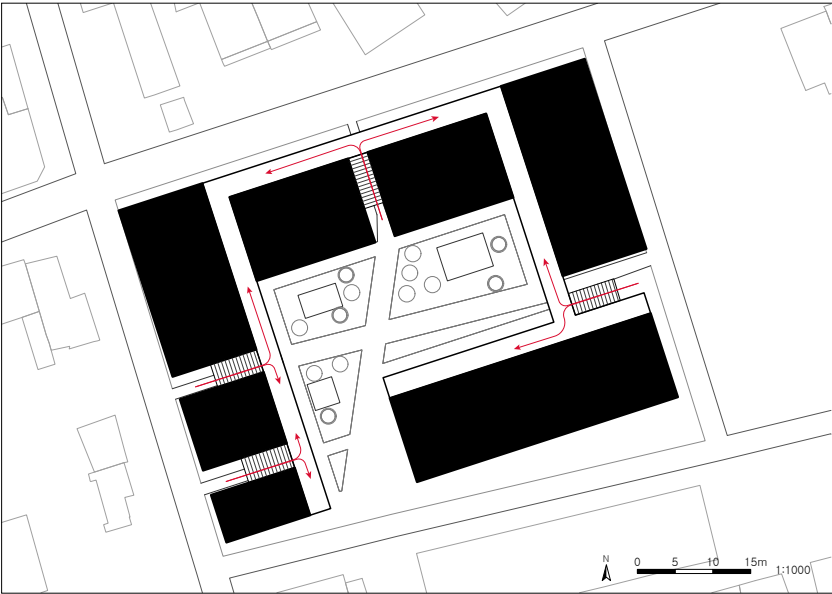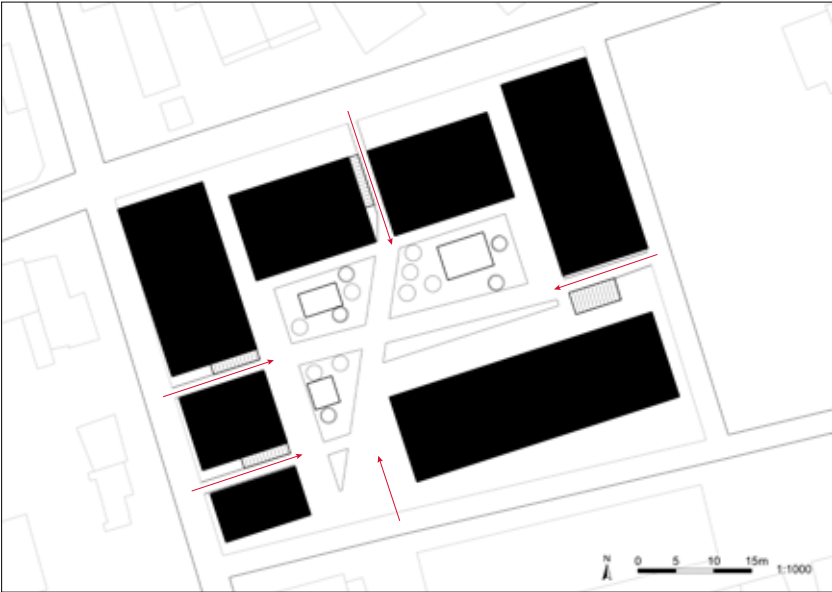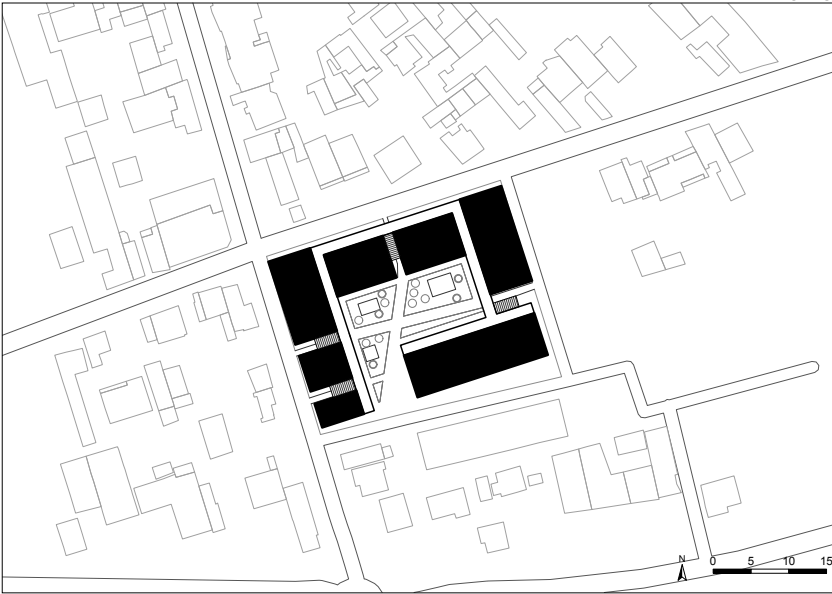


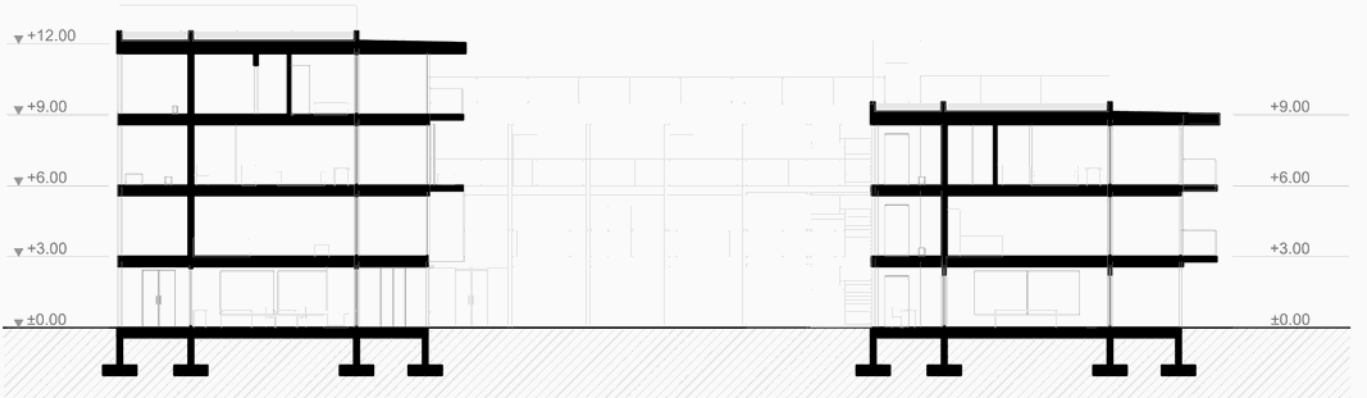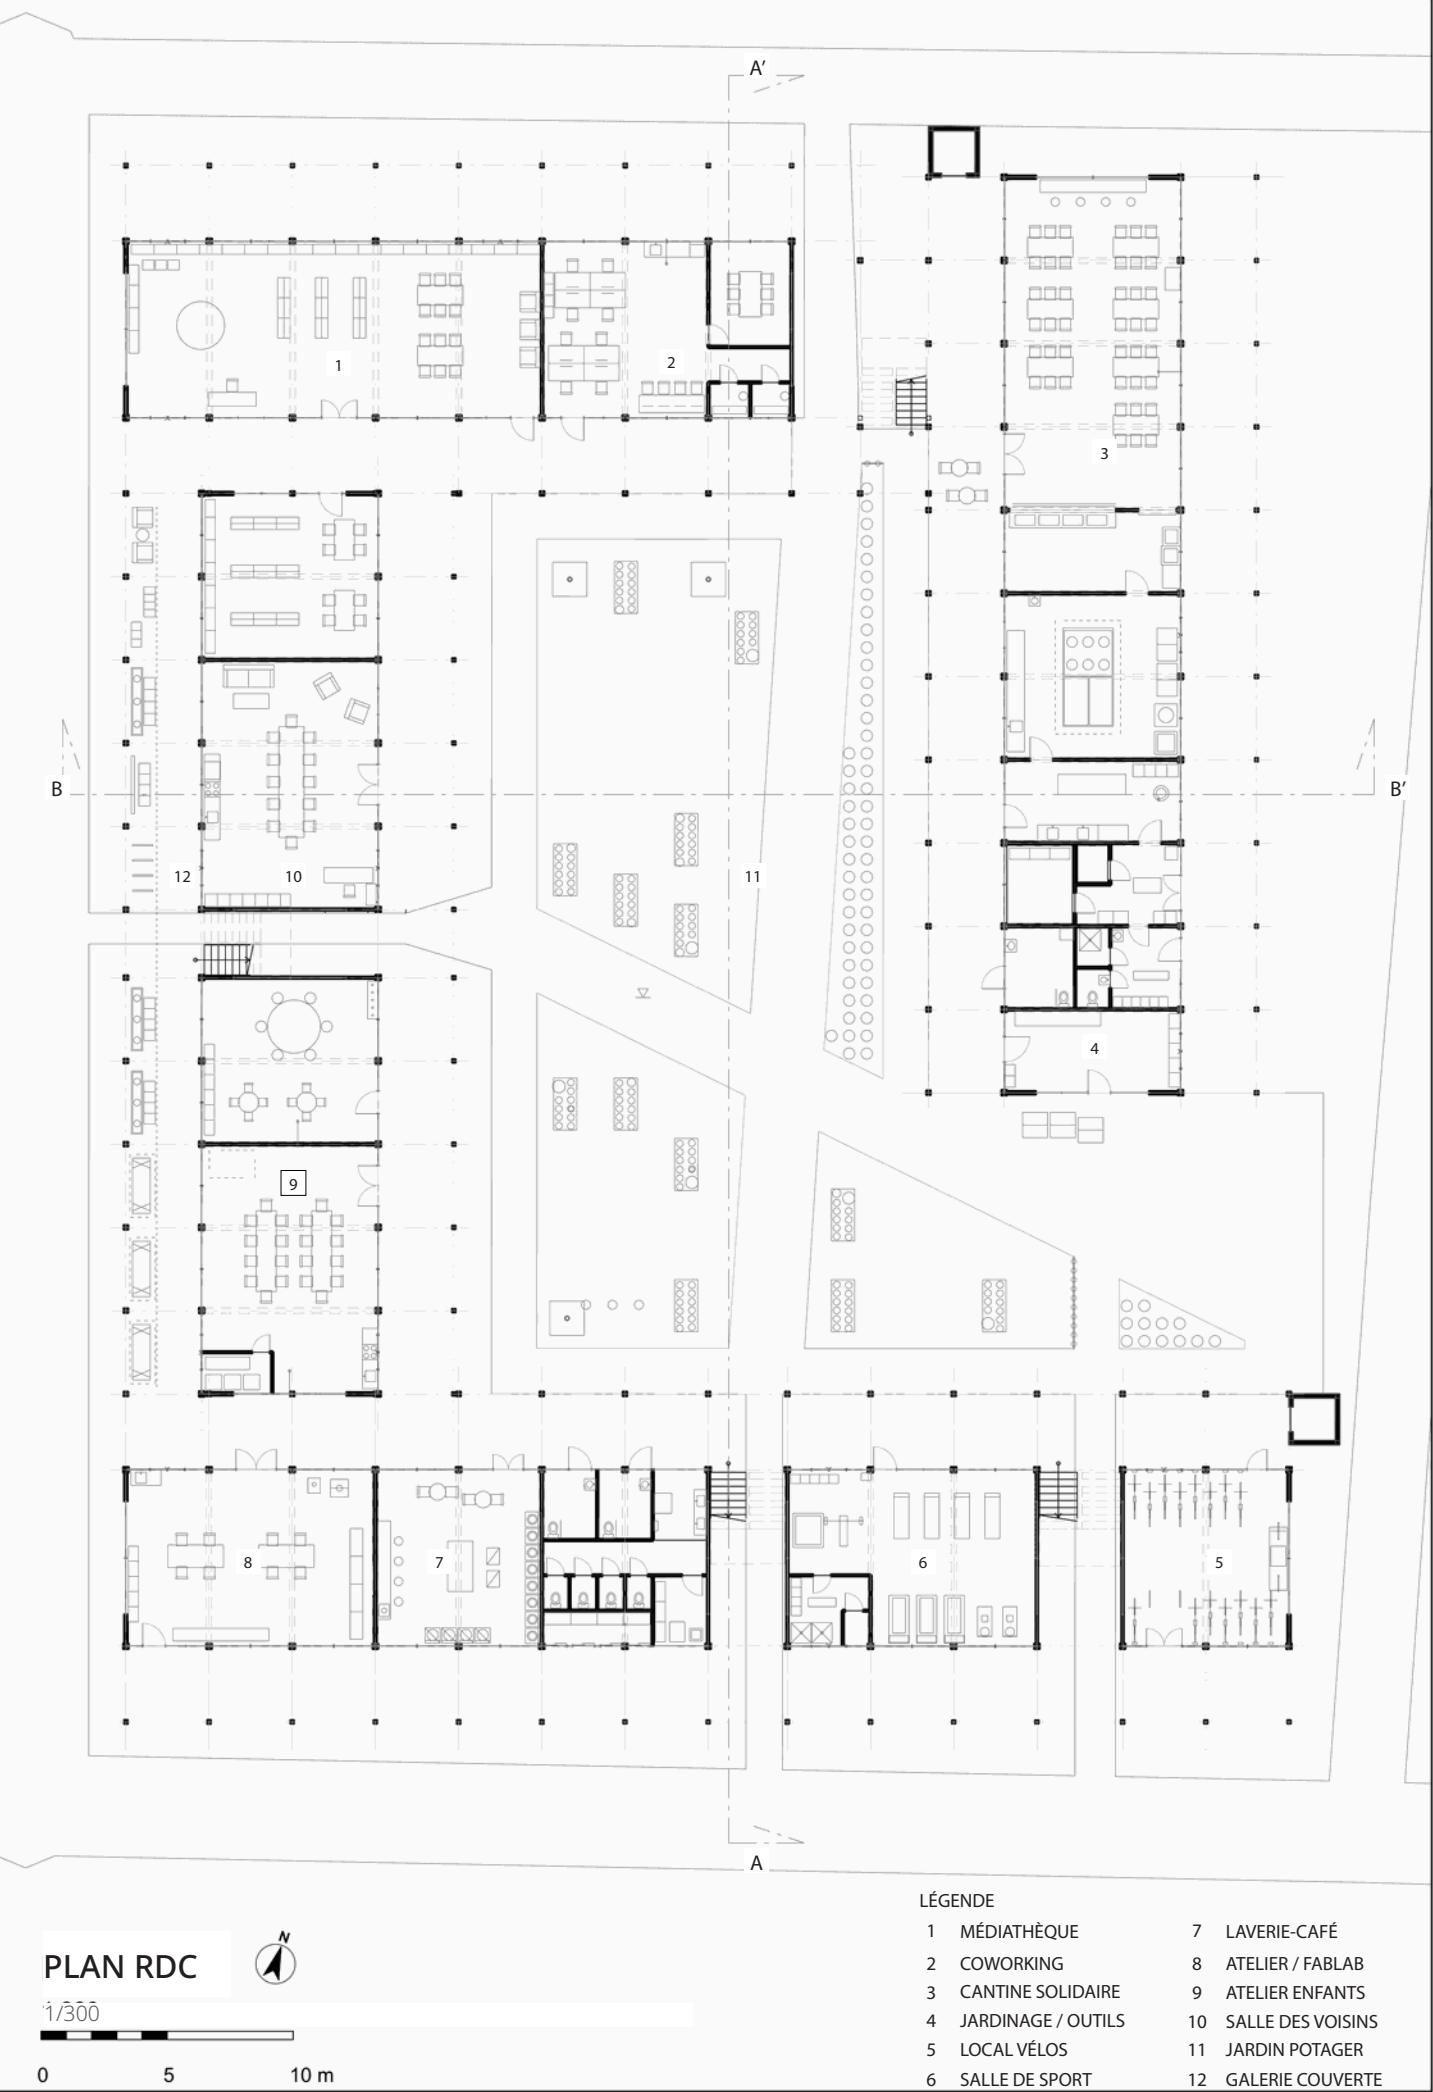

COUPE B - B'


1/300

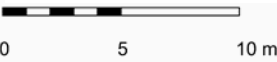

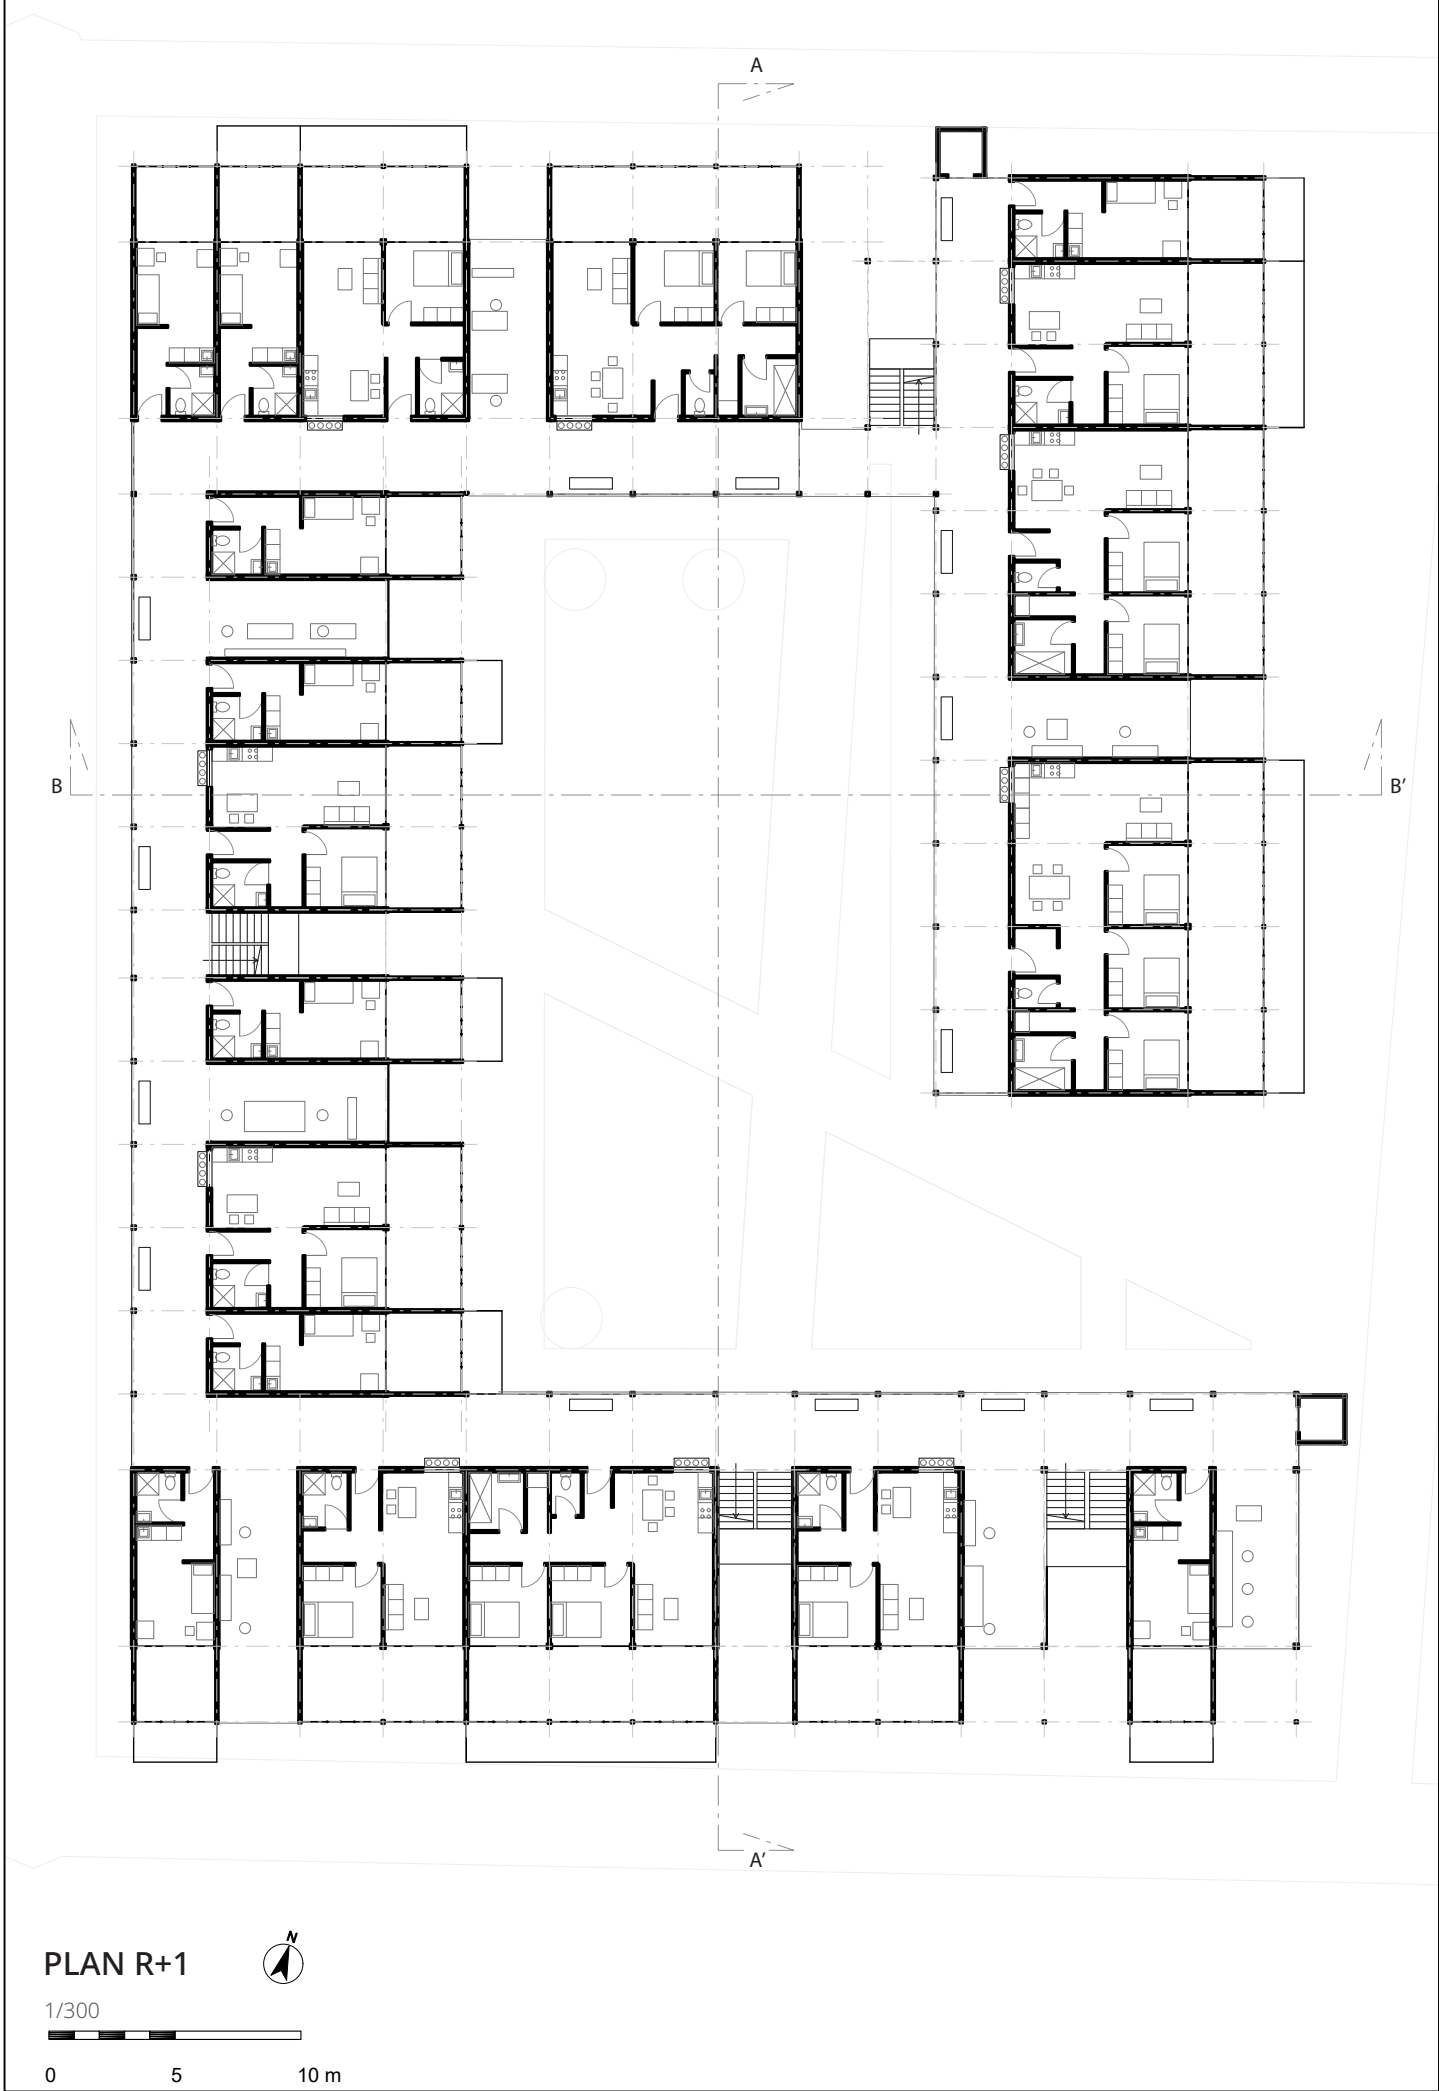

Une trame, plusieurs façons d'habiter


Tout part d'un module de 3,30 × 7 m. Un module donne un studio, deux modules un T2, trois un T3 : les typologies changent, mais la trame reste la même d'un bout à l'autre du bâtiment.

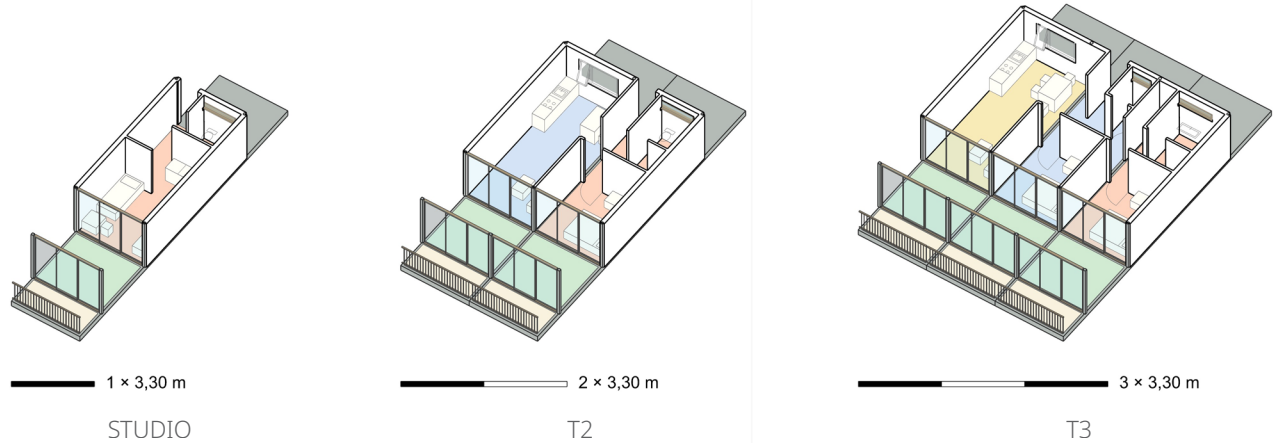

Des espaces qui s'adaptent


La structure porteuse ne bouge pas. Les cloisons séparatives, elles, peuvent être déplacées pour regrouper ou redécouper les logements. Un studio devient un T2 quand la famille s'agrandit ; un T3 se divise quand les enfants partent. Le logement suit ainsi les étapes de la vie de ses habitants.

- LÉGENDE
- Module 1
 - Module 2
 - Module 3
 - Jardin d'hiver
 - Balcon

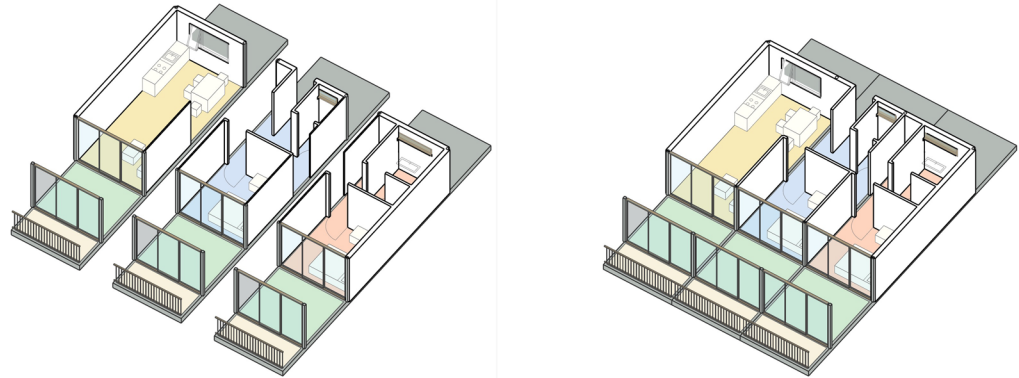


Un jardin d'hiver au fil des saisons

Entre le logement et le balcon, le jardin d'hiver sert d'espace de transition. L'été, ses parois vitrées s'ouvrent en grand et il prolonge le logement vers l'extérieur. L'hiver, elles se referment et il protège l'intérieur du froid.

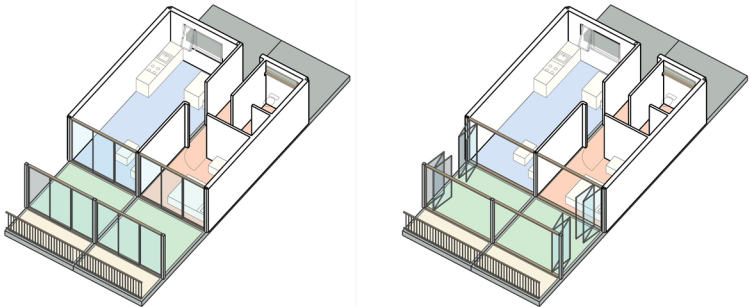


COUPE DE DÉTAIL 1/20

Logement Jardin d'hiver Balcon : Continuité de l'isolation thermique

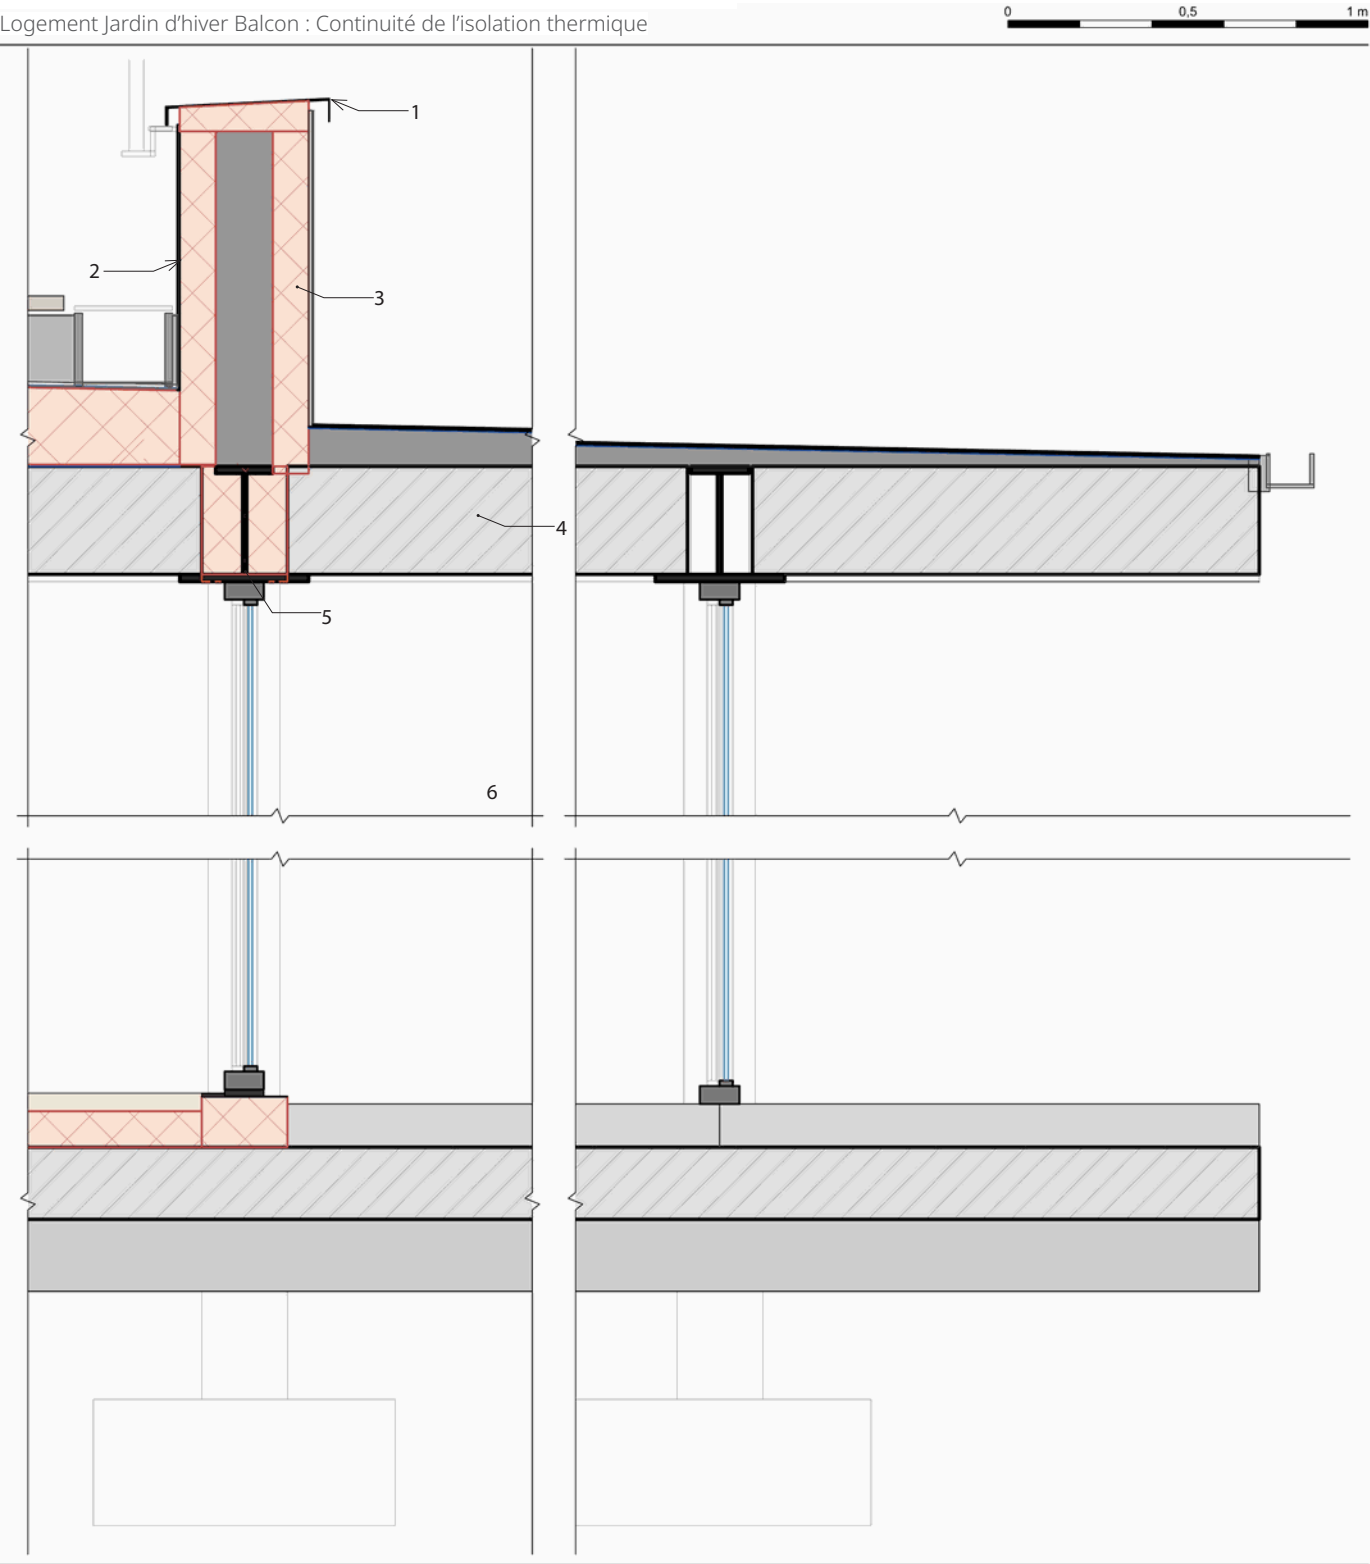

COUPE DE REPÉRAGE 1/250

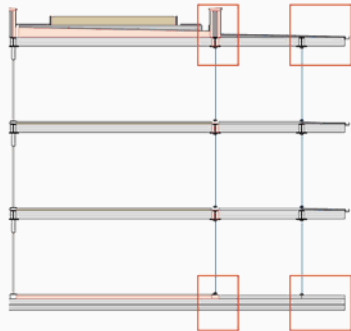

- LÉGENDE
- 1 Couvertine en zinc
 - 2 Isolant thermique
 - 3 Étanchéité
 - 4 Dalle en béton armé
 - 5 Poutre métallique en profilé H
 - 6 Jardin d'hiver

